


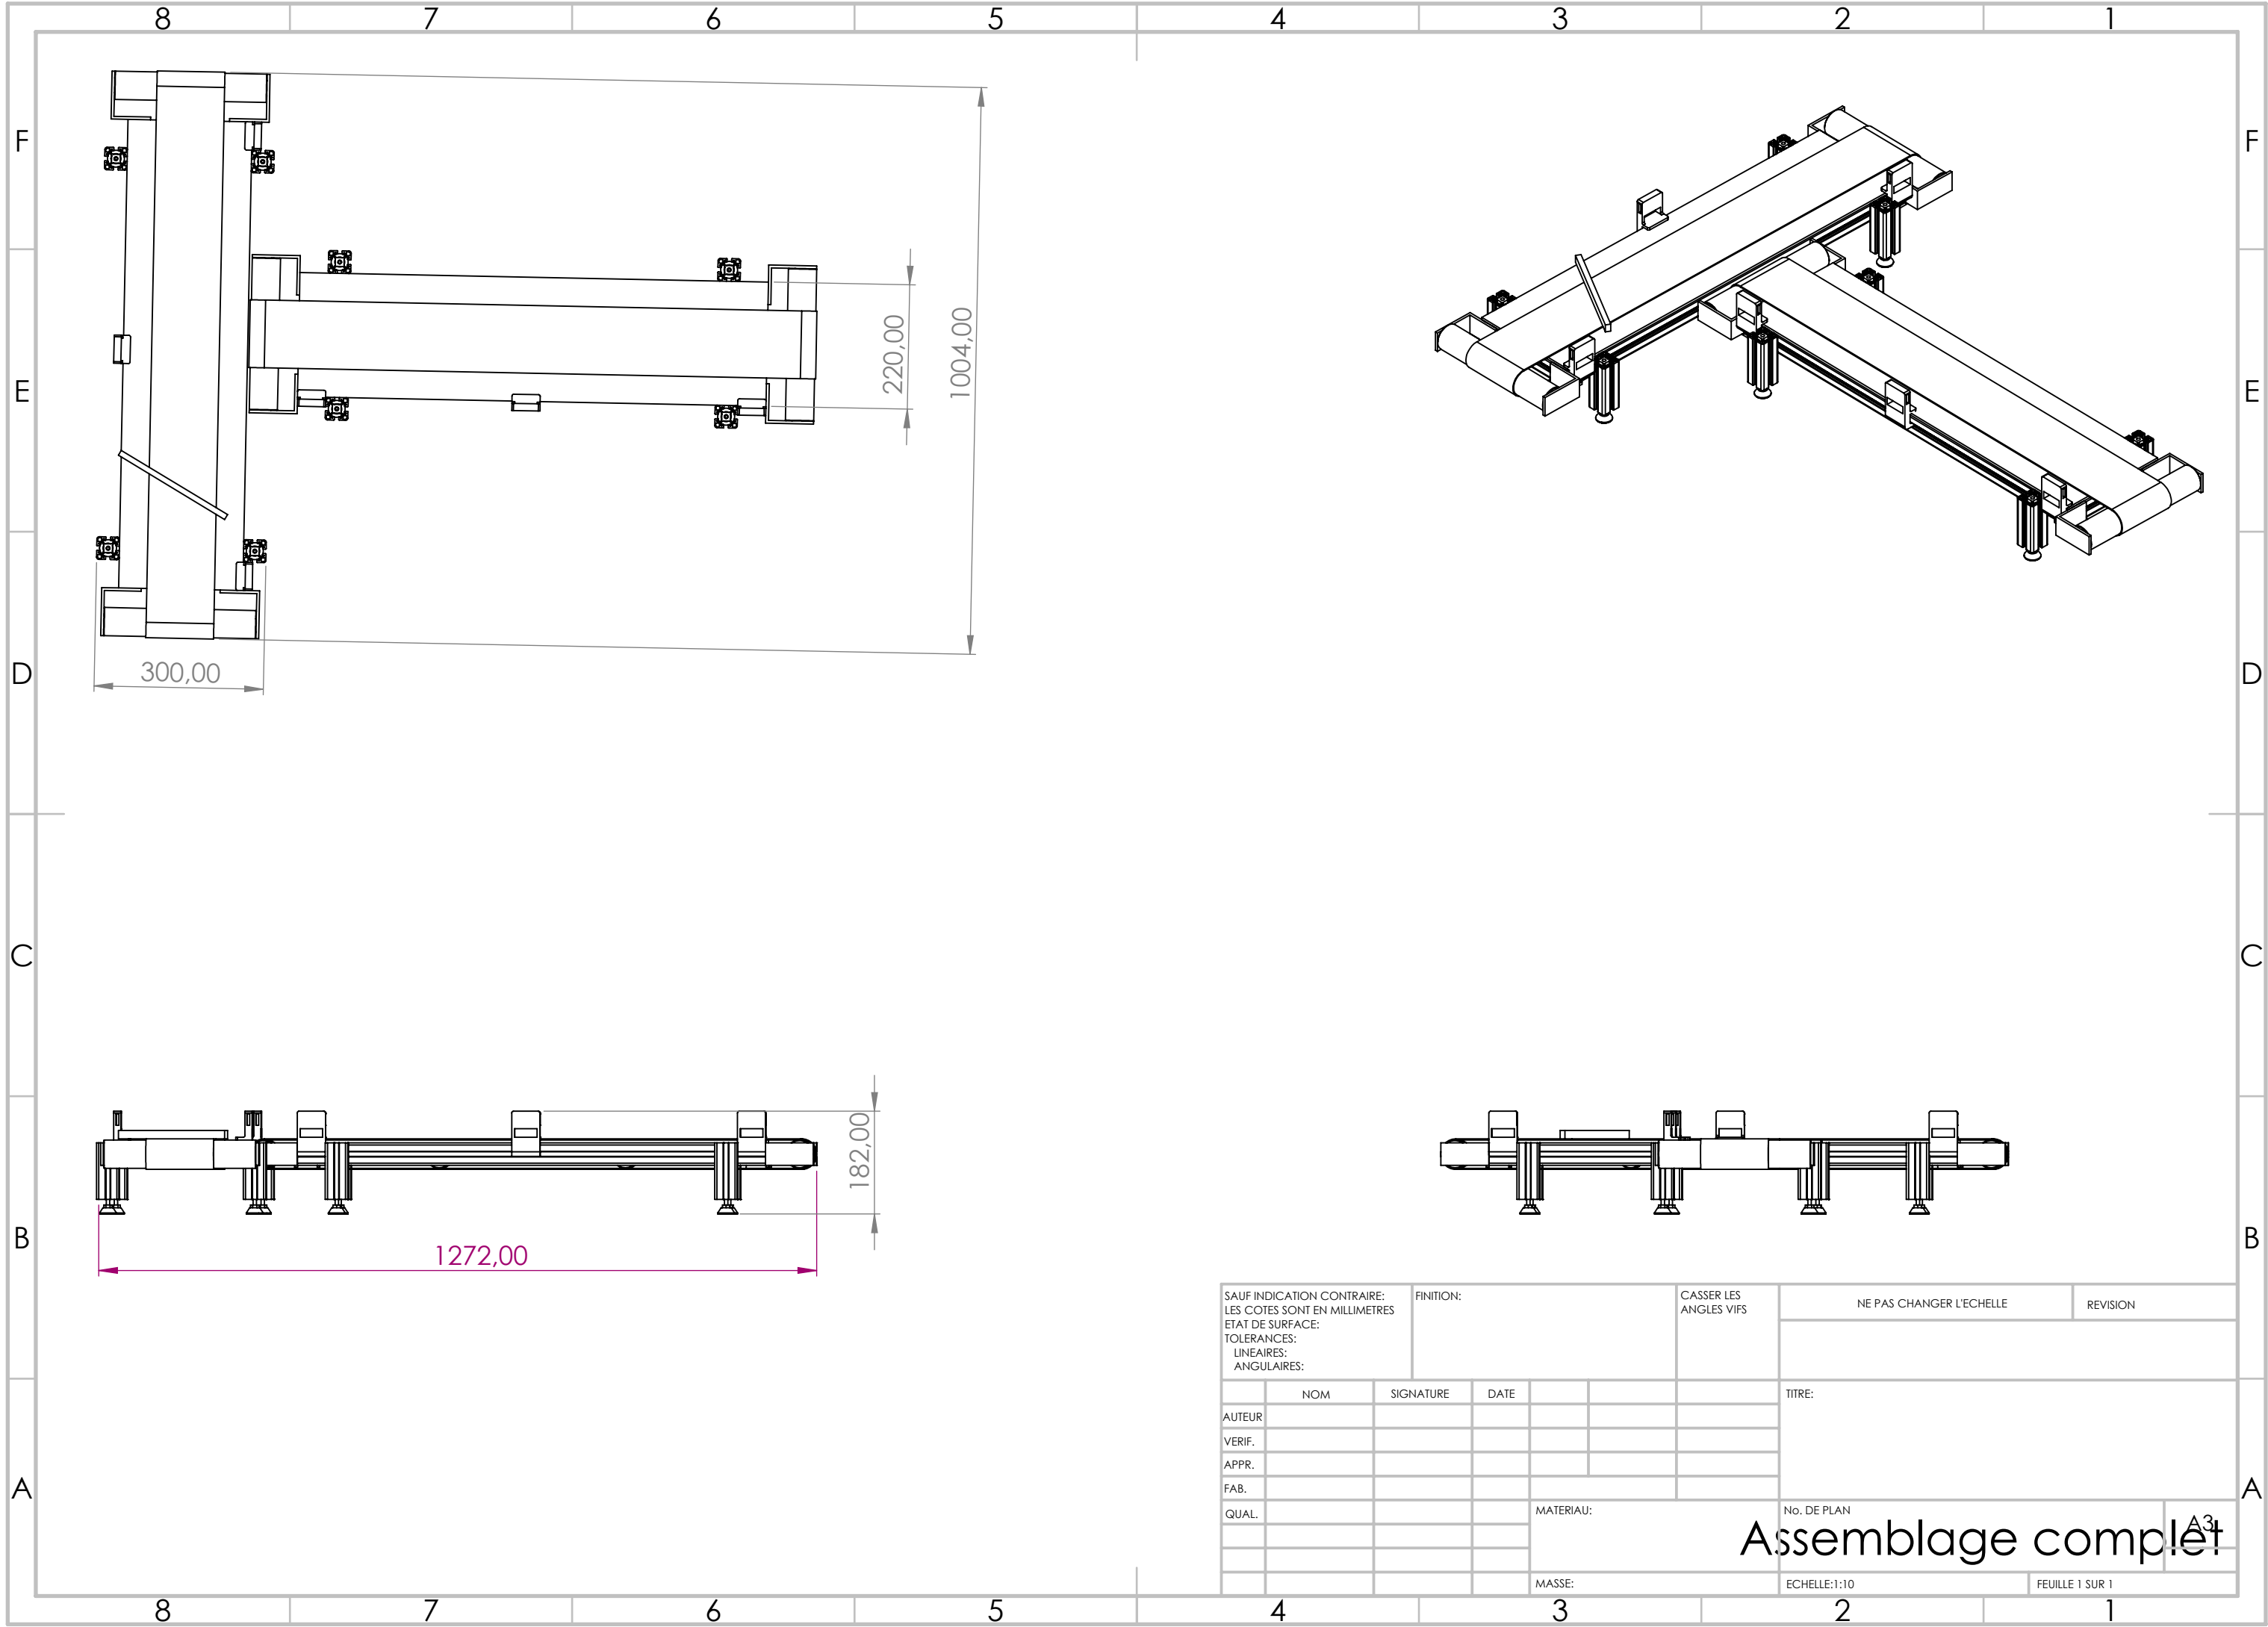

SAUF INDICATION CONTRAIRE: LES COTES SONT EN MILLIMETRES ETAT DE SURFACE: TOLERANCES: LINEAIRES: ANGULAIRES:				FINITION:		CASSER LES ANGLES VIFS		NE PAS CHANGER L'ECHELLE	REVISION
	NOM	SIGNATURE	DATE					TITRE:	
AUTEUR									
VERIF.									
APPR.									
FAB.									
QUAL.								No. DE PLAN	
								Assemblage complet	
								Echelle: 1:10	
								FEUILLE 1 SUR 1	